


SCALE: 1/8" = 1'-0"

LACKLAND CITY SUBDIVISION · SAN ANTONIO, TX. · BEXAR COUNTY

SF 1600 F — CONCEPT STUDY, NOT FOR CONSTRUCTION

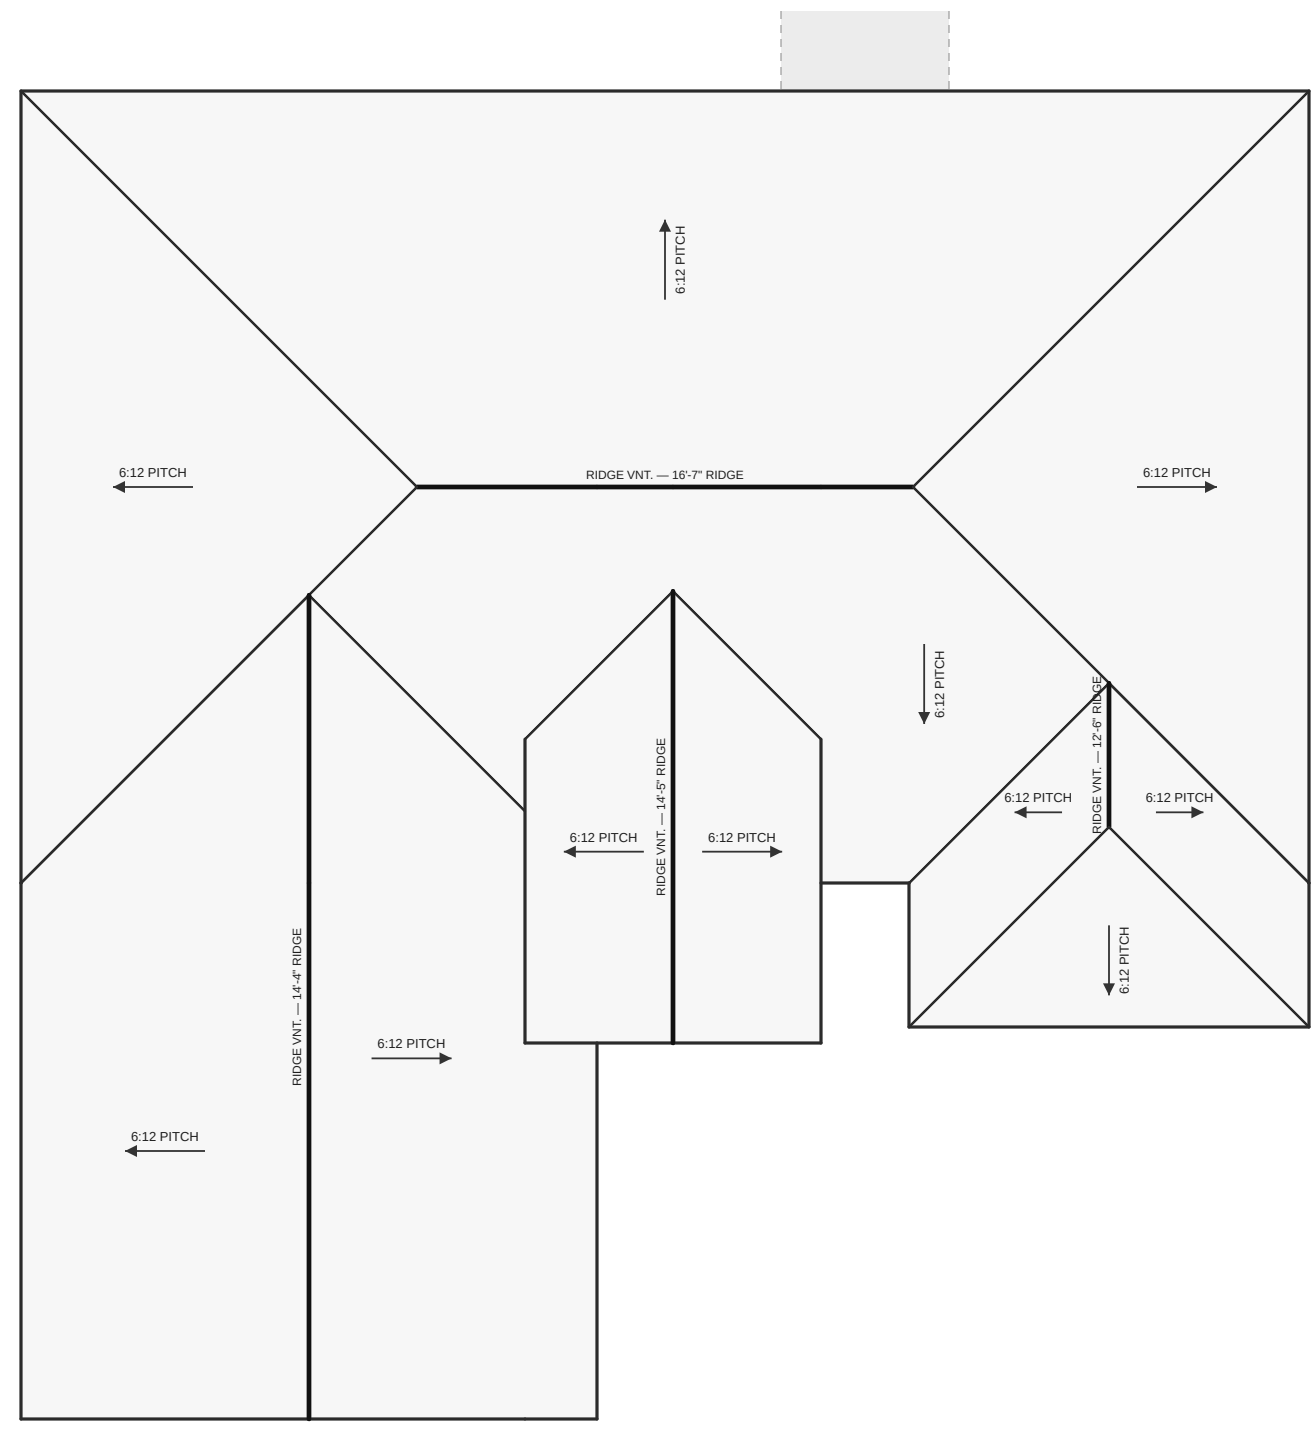

ROOF PLAN
SCALE: 1/8" = 1'-0"

1. All construction to be done according to the 2021 I.R.C. (International Residential Code) and local amendments; tornado resistance per the original plan notes.
2. Make sure all drainage run-off flows away from the house foundation. Provide PVC conduits below driveways for future landscape wiring.
3. All roof overhangs to be 18" from frame unless noted otherwise. Composition shingles, 6:12 pitch, ridge vents. Metal flashing at roof intersections, adjoining walls and roof penetrations.
4. Siding & batton siding as selected with 4" trim, stone veneer wainscot to 3' with brick w/rock cap, as specified.
5. Plaster 1/2", covered porch plate 12-1". Header heights 6'-8". Exterior walls 2x4 with 5/16" veneer ledge as the original; plumbing walls 2x6.
6. Site placement: house set 7'-9 1/2" off the left P.L. and 36'-9 1/2" from the Hunt Lane P.L.; clearances left 7'-9 1/2", right 5'-0", front 20'-10 1/2" (B.S.I. 5' / 5' 10"). Verify against local P.L. and deed restrictions before proceeding.
7. Areas are computed to the outside face of frame from the plan geometry; the original SF 1258 F sheet tabulated 1,258 sf living by its own convention.

MARK	SIZE	TYPE	REMARKS
1	16'-0" x 6'-8"	overhead	16x8 O.H. garage door
2	3068	hinged	3068 front entry w/ 2-1060 fixed sidelights
3	3068	hinged	3068 1-3/8 S.C. w/ closer (garage)
4	2668	french	PR 2668 15-lite french doors
5a	3068	hinged	3068 master bedroom
5b	3068	hinged	3068 master bath
5c	3068	hinged	3068 utility
6	2668	hinged	2668 pantry
7a	2868	hinged	2868 W.I.C.
7b	2868	hinged	2868 bedroom-3
7c	2868	hinged	2868 bath 2
7d	2868	hinged	2868 bedroom-2
7e	2668	double	PR 2668 closet
8	2668	double	PR 2668 closet
9	3010	opening	3010 cased opening
9b	3010	opening	3010 cased opening
10	2068	bifold	2068 bifold linen & hamper
11	2'-8" x 6'-8"	hinged	32 in. glass shower door


MARK	UNIT	QTY	ROUGH WIDTH	REMARKS
A	PR 3050 SH	3	6'-0"	Vinyl, insul, low-E glass, screens; SHGC .25 / U .35 max; tempered where required (IRC R308)
B	3030 SH safety glz	1	3'-0"	Vinyl, insul, low-E glass, screens; SHGC .25 / U .35 max; tempered where required (IRC R308)
C	PR 2050 SH	1	4'-0"	Vinyl, insul, low-E glass, screens; SHGC .25 / U .35 max; tempered where required (IRC R308)
D	3010 HS	2	3'-0"	Vinyl, insul, low-E glass, screens; SHGC .25 / U .35 max; tempered where required (IRC R308)
E	1060 fixed sidelight	2	1'-0"	Vinyl, insul, low-E glass, screens; SHGC .25 / U .35 max; tempered where required (IRC R308)

Notes: see manufacturer for rough openings; window brand as selected by owner; every bedroom has an egress window (PR 3050 SH).

IMPERVIOUS COVER	
LOT	7,286
HOUSE	2,133
FLATWORK	479
TOTAL	2,612 (36%)


1

SHEET OF 2

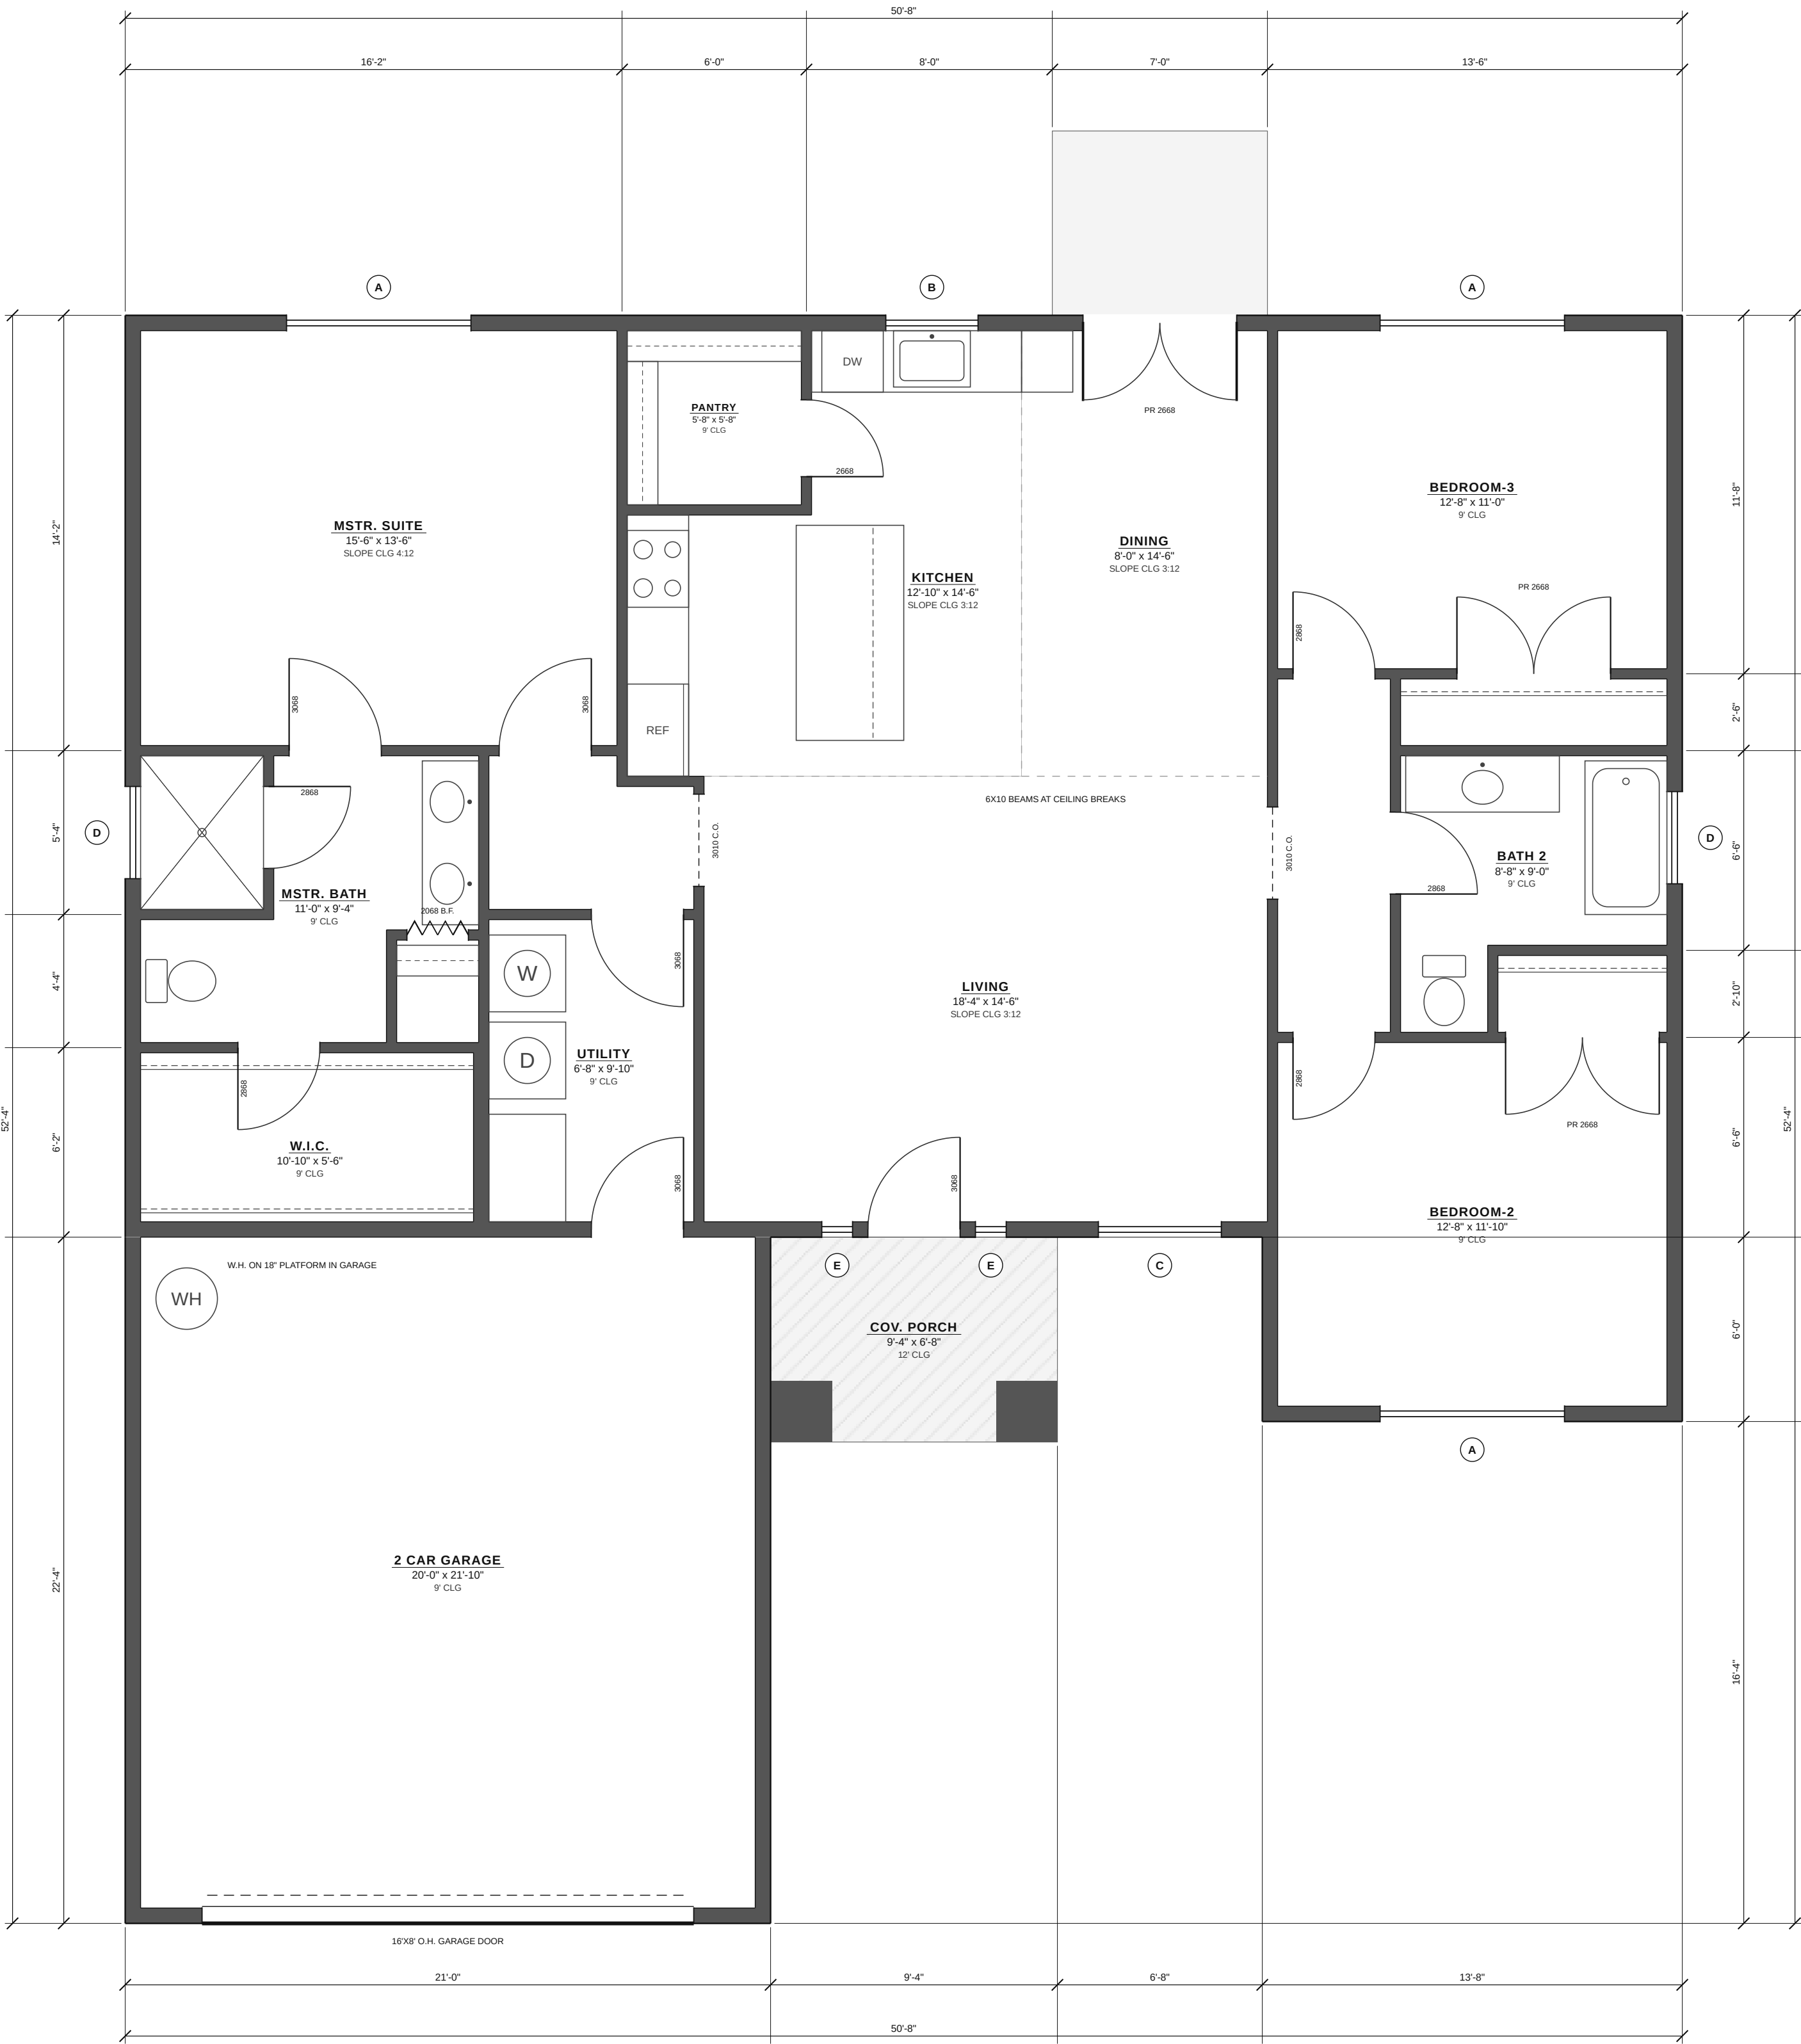


FLOOR PLAN
SCALE: 1/4" = 1'-0"


LIVING AREA	1,902 SF
GARAGE	469 SF
PORCH	62 SF
TOTAL UNDER ROOF	2,133 SF

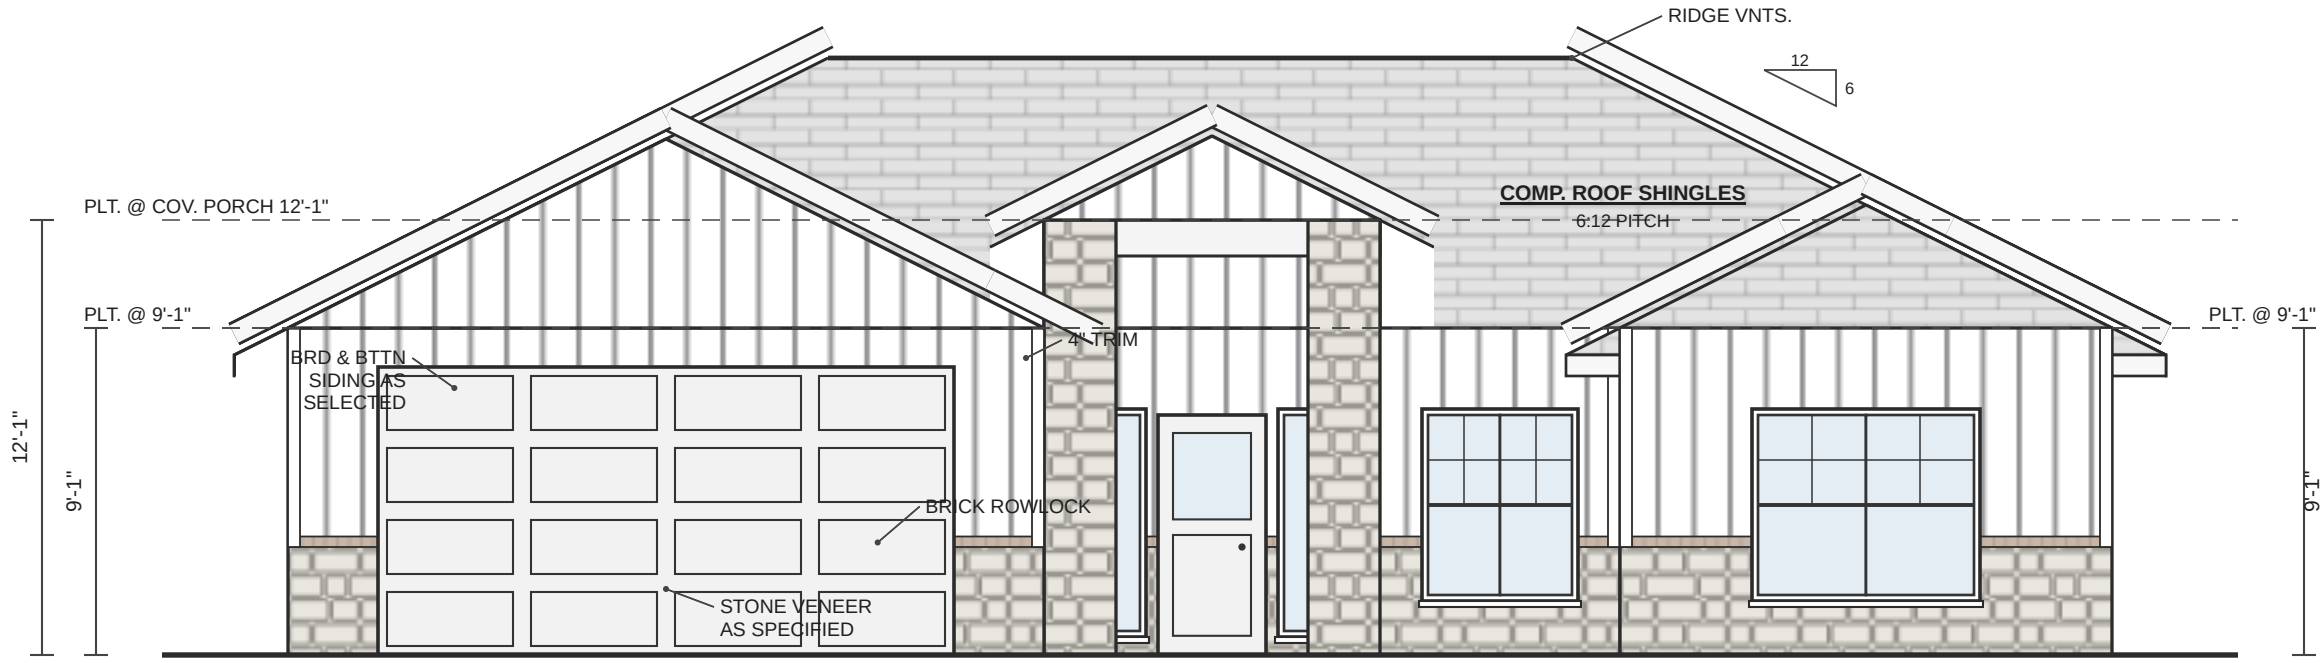


FRONT ELEVATION
SCALE: 3/16" = 1'-0"

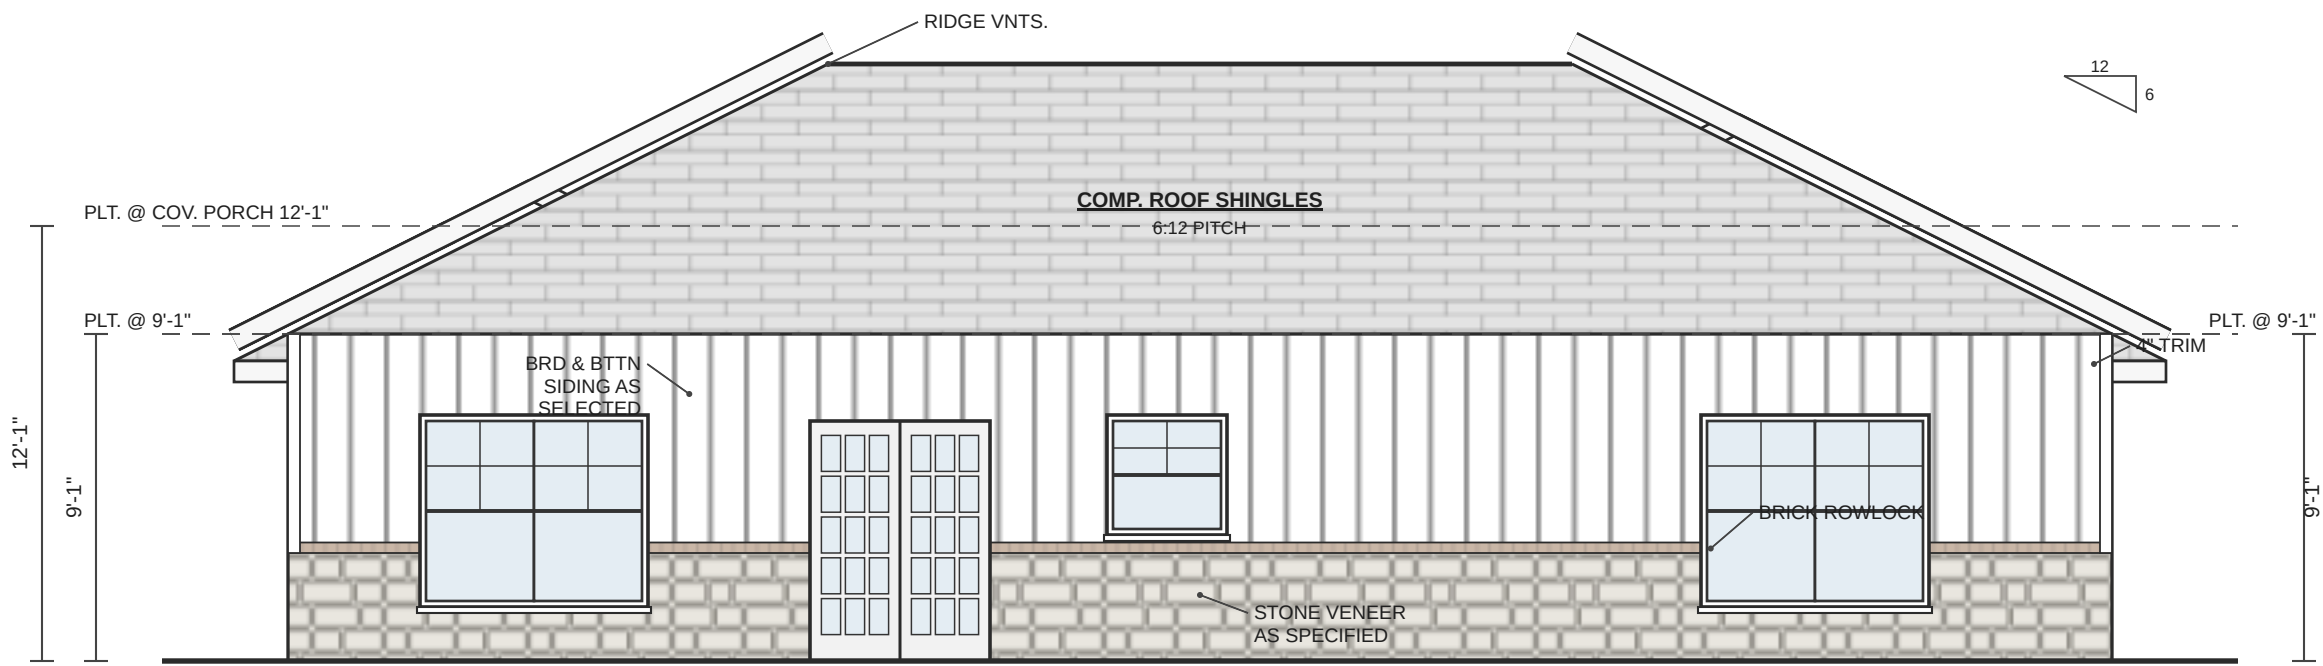

REAR ELEVATION
SCALE: 3/16" = 1'-0"

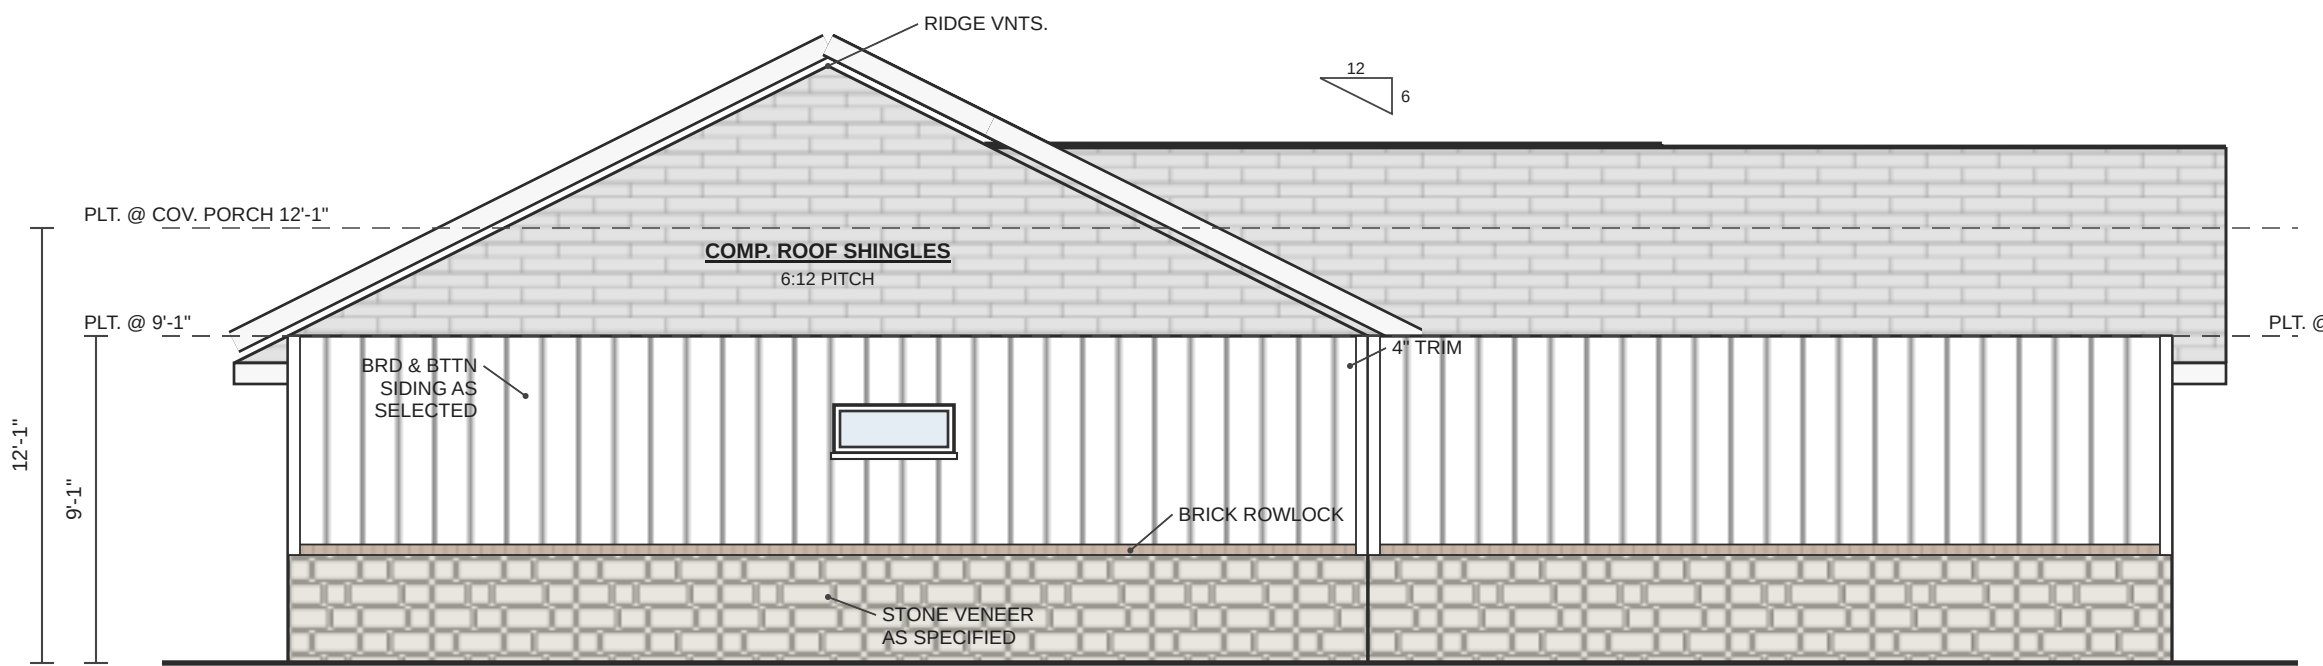

LEFT ELEVATION
SCALE: 3/16" = 1'-0"

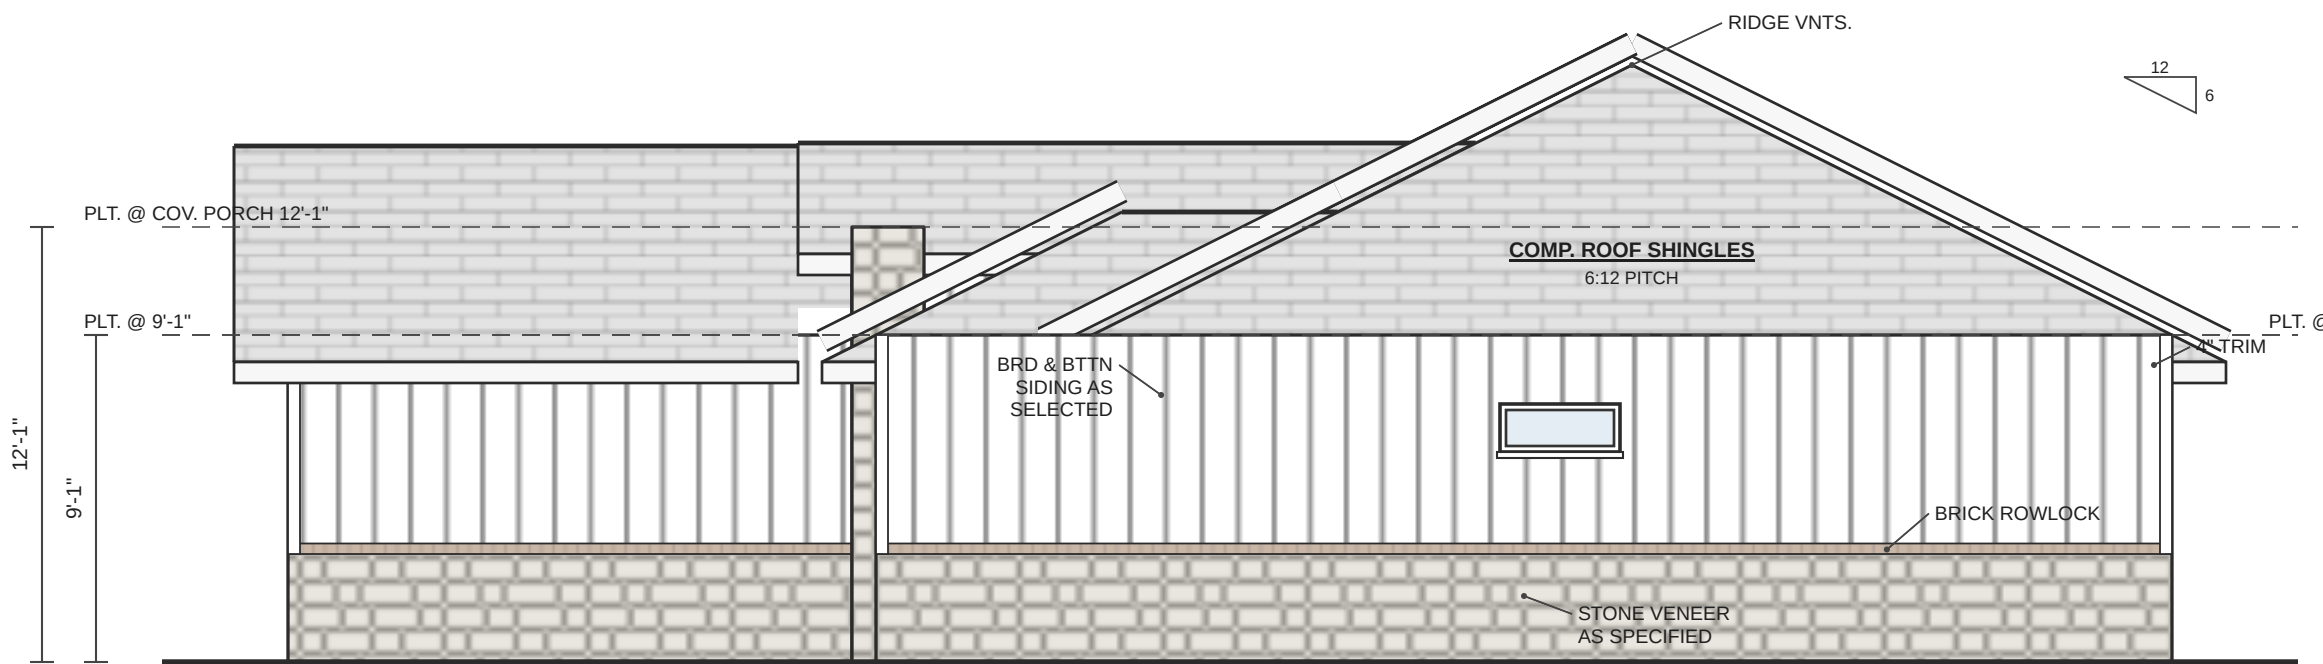

RIGHT ELEVATION
SCALE: 3/16" = 1'-0"

SF 1600 F

1,600 SF VARIANT OF SF 1258 F

CONCEPT STUDY
NOT FOR CONSTRUCTION

DERIVED FROM
Plan Factory plan SF 1258 "F" — designs by
Antonio Escobedo, San Antonio, TX (drawn
6/22/2023, plotted 10/10/2023). Permit
drawings must be prepared by the plan's
designer or a licensed designer/engineer.

PREPARED FOR
DANTEGA HOMES
DANIEL ORHIUNU
738 SAWTOOTH DR.
Lot 48 - Block 23 - N.C.B. 15850
Lackland City Subdivision
San Antonio, Bexar County, TX

SQUARE FOOTAGE TABULATIONS	
LIVING AREA	1,602
GARAGE	469
COV. PORCH	62
TOTAL UNDER ROOF	2,133
FLATWORK	479

FLOOR PLAN & ELEVATIONS

DATE
2026-09-04
GENERATED FROM
plans/sf1600/spec/sf1600.json - 2021 IRC
conventions carried from the original sheets