


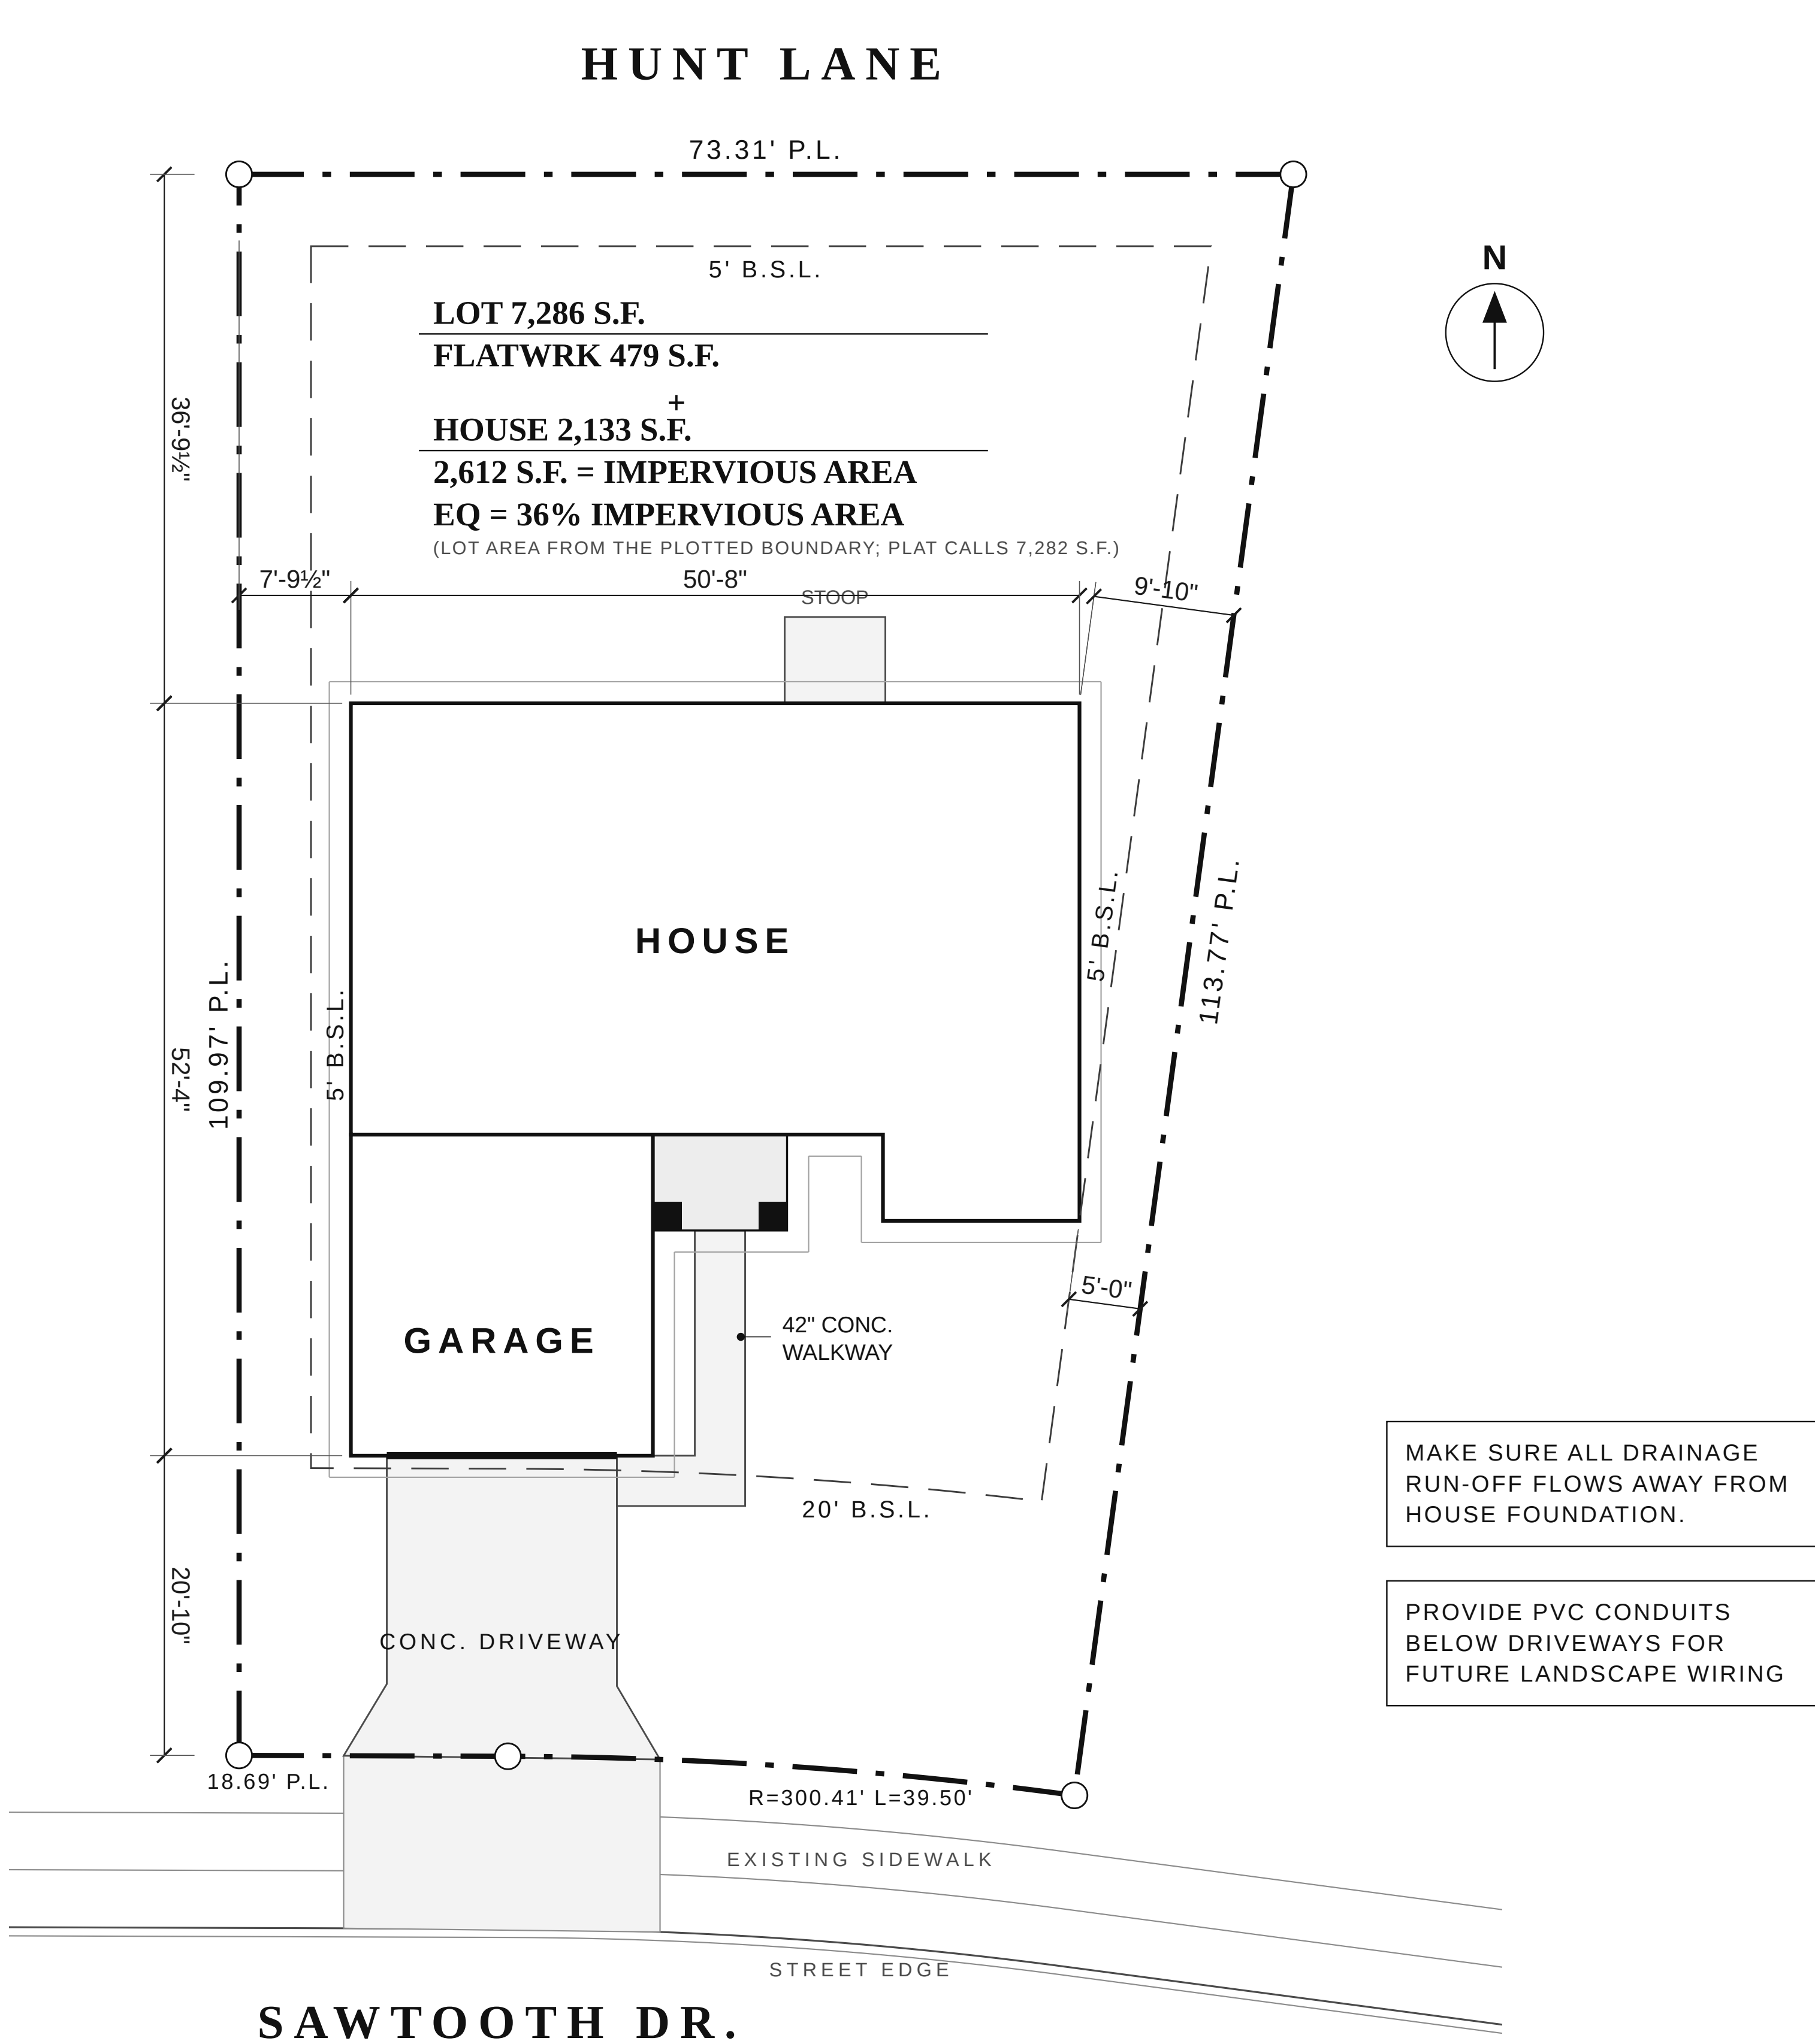

SITE PLAN


SCALE: 1/8" = 1'-0"

CLEARANCES TO P.L.: LEFT 7'-9½" RIGHT 5'-0" REAR 36'-9½" FRONT 20'-10½" (REQ'D 5' / 5' / 5' / 20')

738 SAWTOOTH DR. · LOT 48 · BLOCK 23 · N.C.B. 15850

LACKLAND CITY SUBDIVISION · SAN ANTONIO, TX. · BEXAR COUNTY

SF 1600 F — CONCEPT STUDY, NOT FOR CONSTRUCTION

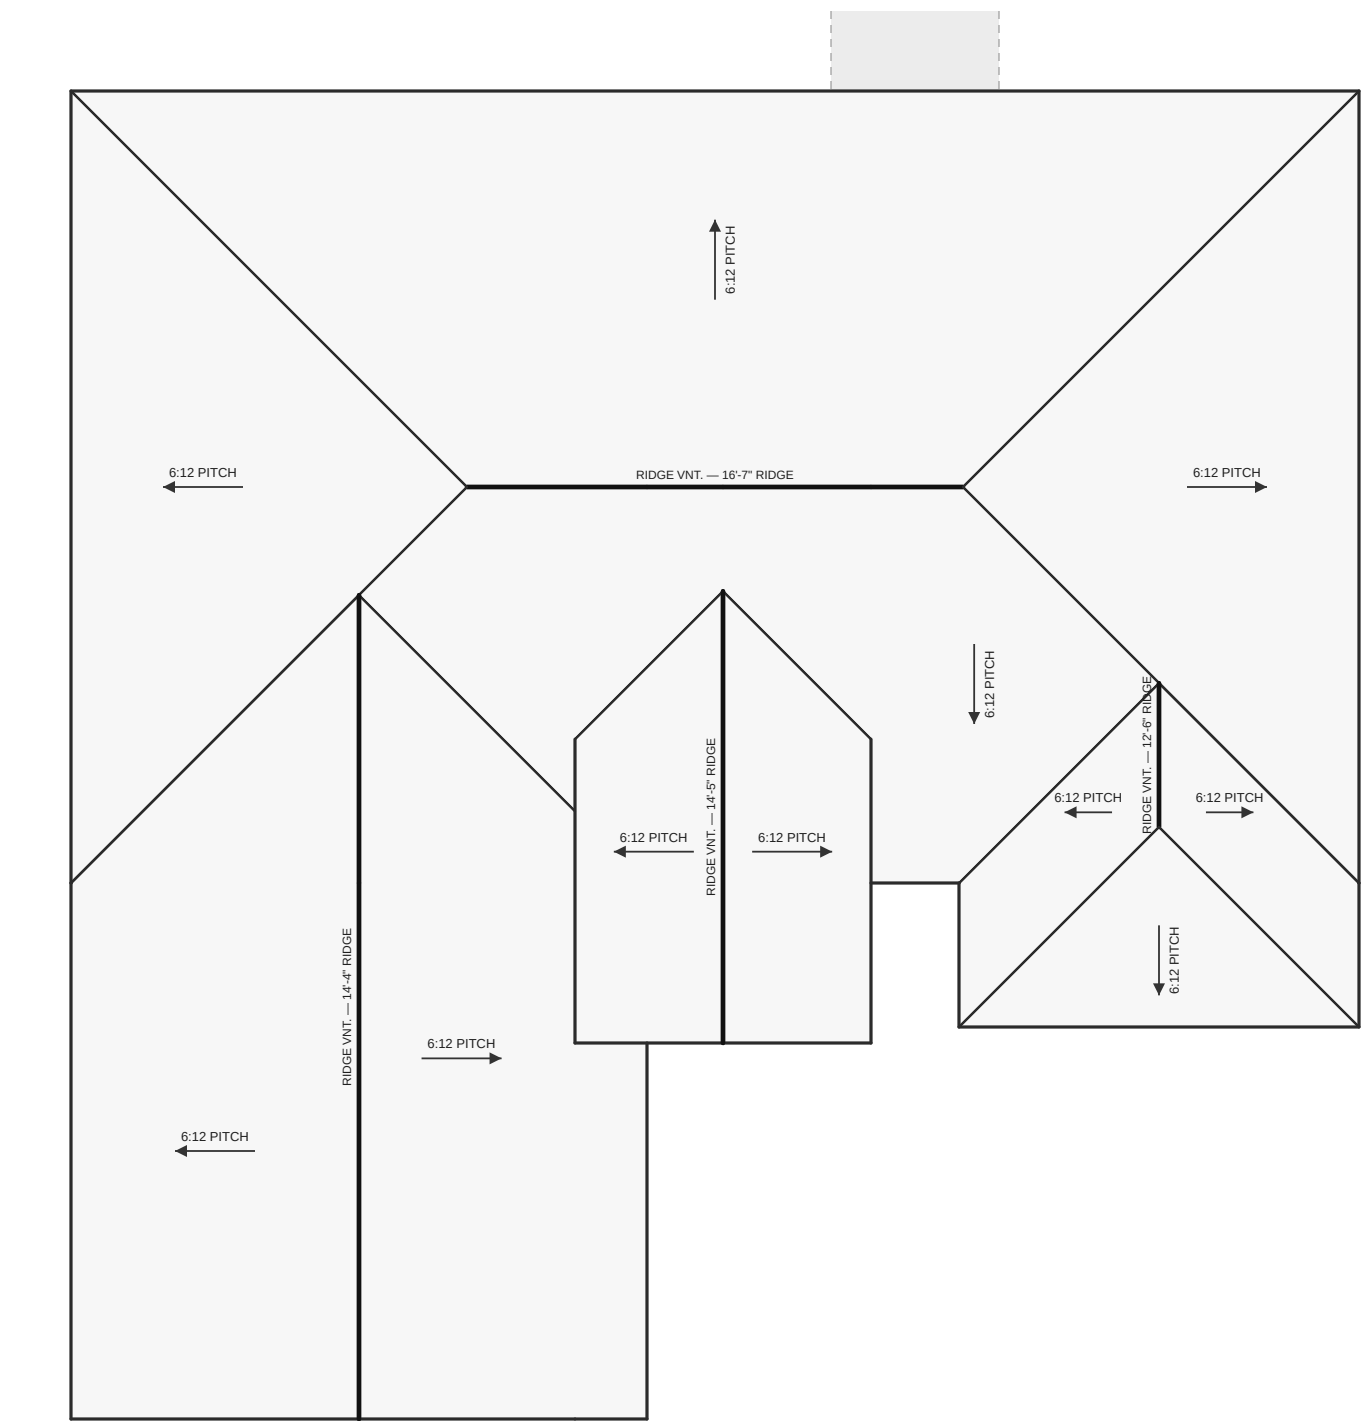

NOTE: ALL ROOF OVERHANGS TO BE 18" FROM FRAME, UNLESS NOTED OTHERWISE.
1. NAILS FOR SECURING SHINGLES SHALL BE CORROSION RESISTANT. 2. METAL FLASHING SHALL BE PROVIDED AT ROOF INTERSECTIONS, ADJOINING WALLS AND PROJECTIONS THRU ROOF.
6:12 PITCH ALL PLANES · COMPOSITION SHINGLES · RIDGE VENTS · PLATE 9'-0" (CON. PORCH 12'-0")

ROOF PLAN

SCALE: 3/8" = 1'-0"

GENERAL NOTES

- All construction to be done according to the 2021 I.R.C. (International Residential Code) and local amendments; tornado resistance per the original plan notes.
- Make sure all drainage run-off flows away from the house foundation. Provide PVC conduits below driveways for future landscape wiring.
- All roof overhangs to be 18" from frame unless noted otherwise. Composition shingles, 6:12 pitch, ridge vents. Metal flashing at roof intersections, adjoining walls and roof penetrations.
- Board & batten siding as selected with 4" trim; stone veneer wainscot to 3'-0" with brick rowlock cap, as specified.
- Plates 9'-1": covered porch plate 12'-1". Header heights 6'-8". Exterior walls 2x4 with 5-1/2" veneer ledge as the original; plumbing walls 2x6.
- Site placement: house set 7'-9½" off the left P.L. and 36'-9½" from the Hunt Lane P.L.; clearances left 7'-9½", right 5'-0", front 20'-10½" (B.S.L. 5' / 5' / 20'). Verify against the recorded plat and deed restrictions before proceeding.
- Areas are computed to the outside face of frame from the plan geometry; the original SF 1258 F sheet tabulated 1,258 sf living by its own convention.

DOOR SCHEDULE

MARK	SIZE	TYPE	REMARKS
1	16'-0" x 6'-8"	overhead	16'x8' O.H. garage door
2	3068	hinged	3068 front entry w/ 2-1060 fixed sidelights
3	3068	hinged	3068 1-3/8 S.C. w/ closer (garage)
4	2668	french	PR 2668 15-lite french doors
5a	3068	hinged	3068 master bedroom
5b	3068	hinged	3068 master bath
5c	3068	hinged	3068 utility
6	2668	hinged	2668 pantry
7a	2868	hinged	2868 W.I.C.
7b	2868	hinged	2868 bedroom-3
7c	2868	hinged	2868 bath 2
7d	2868	hinged	2868 bedroom-2
7e	2668	double	PR 2668 closet
8	2668	double	PR 2668 closet
9	3010	opening	3010 cased opening
9b	3010	opening	3010 cased opening
10	2068	bifold	2068 bifold linen & hamper
11	2'-8" x 6'-8"	hinged	32 in. glass shower door

WINDOW SCHEDULE

MARK	UNIT	QTY	ROUGH WIDTH	REMARKS
A	PR 3050 SH	3	6'-0"	Vinyl, insul, low-E glass, screens, SHGC .25 / U .35 max; tempered where required (IRC R308)
B	3030 SH safety glz	1	3'-0"	Vinyl, insul, low-E glass, screens, SHGC .25 / U .35 max; tempered where required (IRC R308)
C	PR 2050 SH	1	4'-0"	Vinyl, insul, low-E glass, screens, SHGC .25 / U .35 max; tempered where required (IRC R308)
D	3010 HS	2	3'-0"	Vinyl, insul, low-E glass, screens, SHGC .25 / U .35 max; tempered where required (IRC R308)
E	1060 fixed sidelight	2	1'-0"	Vinyl, insul, low-E glass, screens, SHGC .25 / U .35 max; tempered where required (IRC R308)

Notes: see manufacturer for rough openings; window brand as selected by owner; every bedroom has an egress window (PR 3050 SH).

SF 1600 F

1,600 SF VARIANT OF SF 1258 F

CONCEPT STUDY NOT FOR CONSTRUCTION

DERIVED FROM
Plan Factory plan SF 1258 "F" — designs by
Antonio Escobedo, San Antonio, TX (drawn
6/22/2023, plotted 10/10/2023). Permit
drawings must be prepared by the plan's
designer or a licensed designer/engineer.

PREPARED FOR
DANTEGA HOMES
DANIEL ORHIUNO
738 SAWTOOTH DR.
Lot 48 · Block 23 · N.C.B. 15850
Lackland City Subdivision
San Antonio, Bexar County, TX

IMPERVIOUS COVER	
LOT	7,286
HOUSE	2,133
FLATWORK	479
TOTAL	2,612 (36%)

SITE PLAN ROOF PLAN & SCHEDULES


DATE
2026-09-04

GENERATED FROM
plans/sf1600/spec/sf1600.json · 2021 IRC
conventions carried from the original sheets

SHEET


1

OF 2

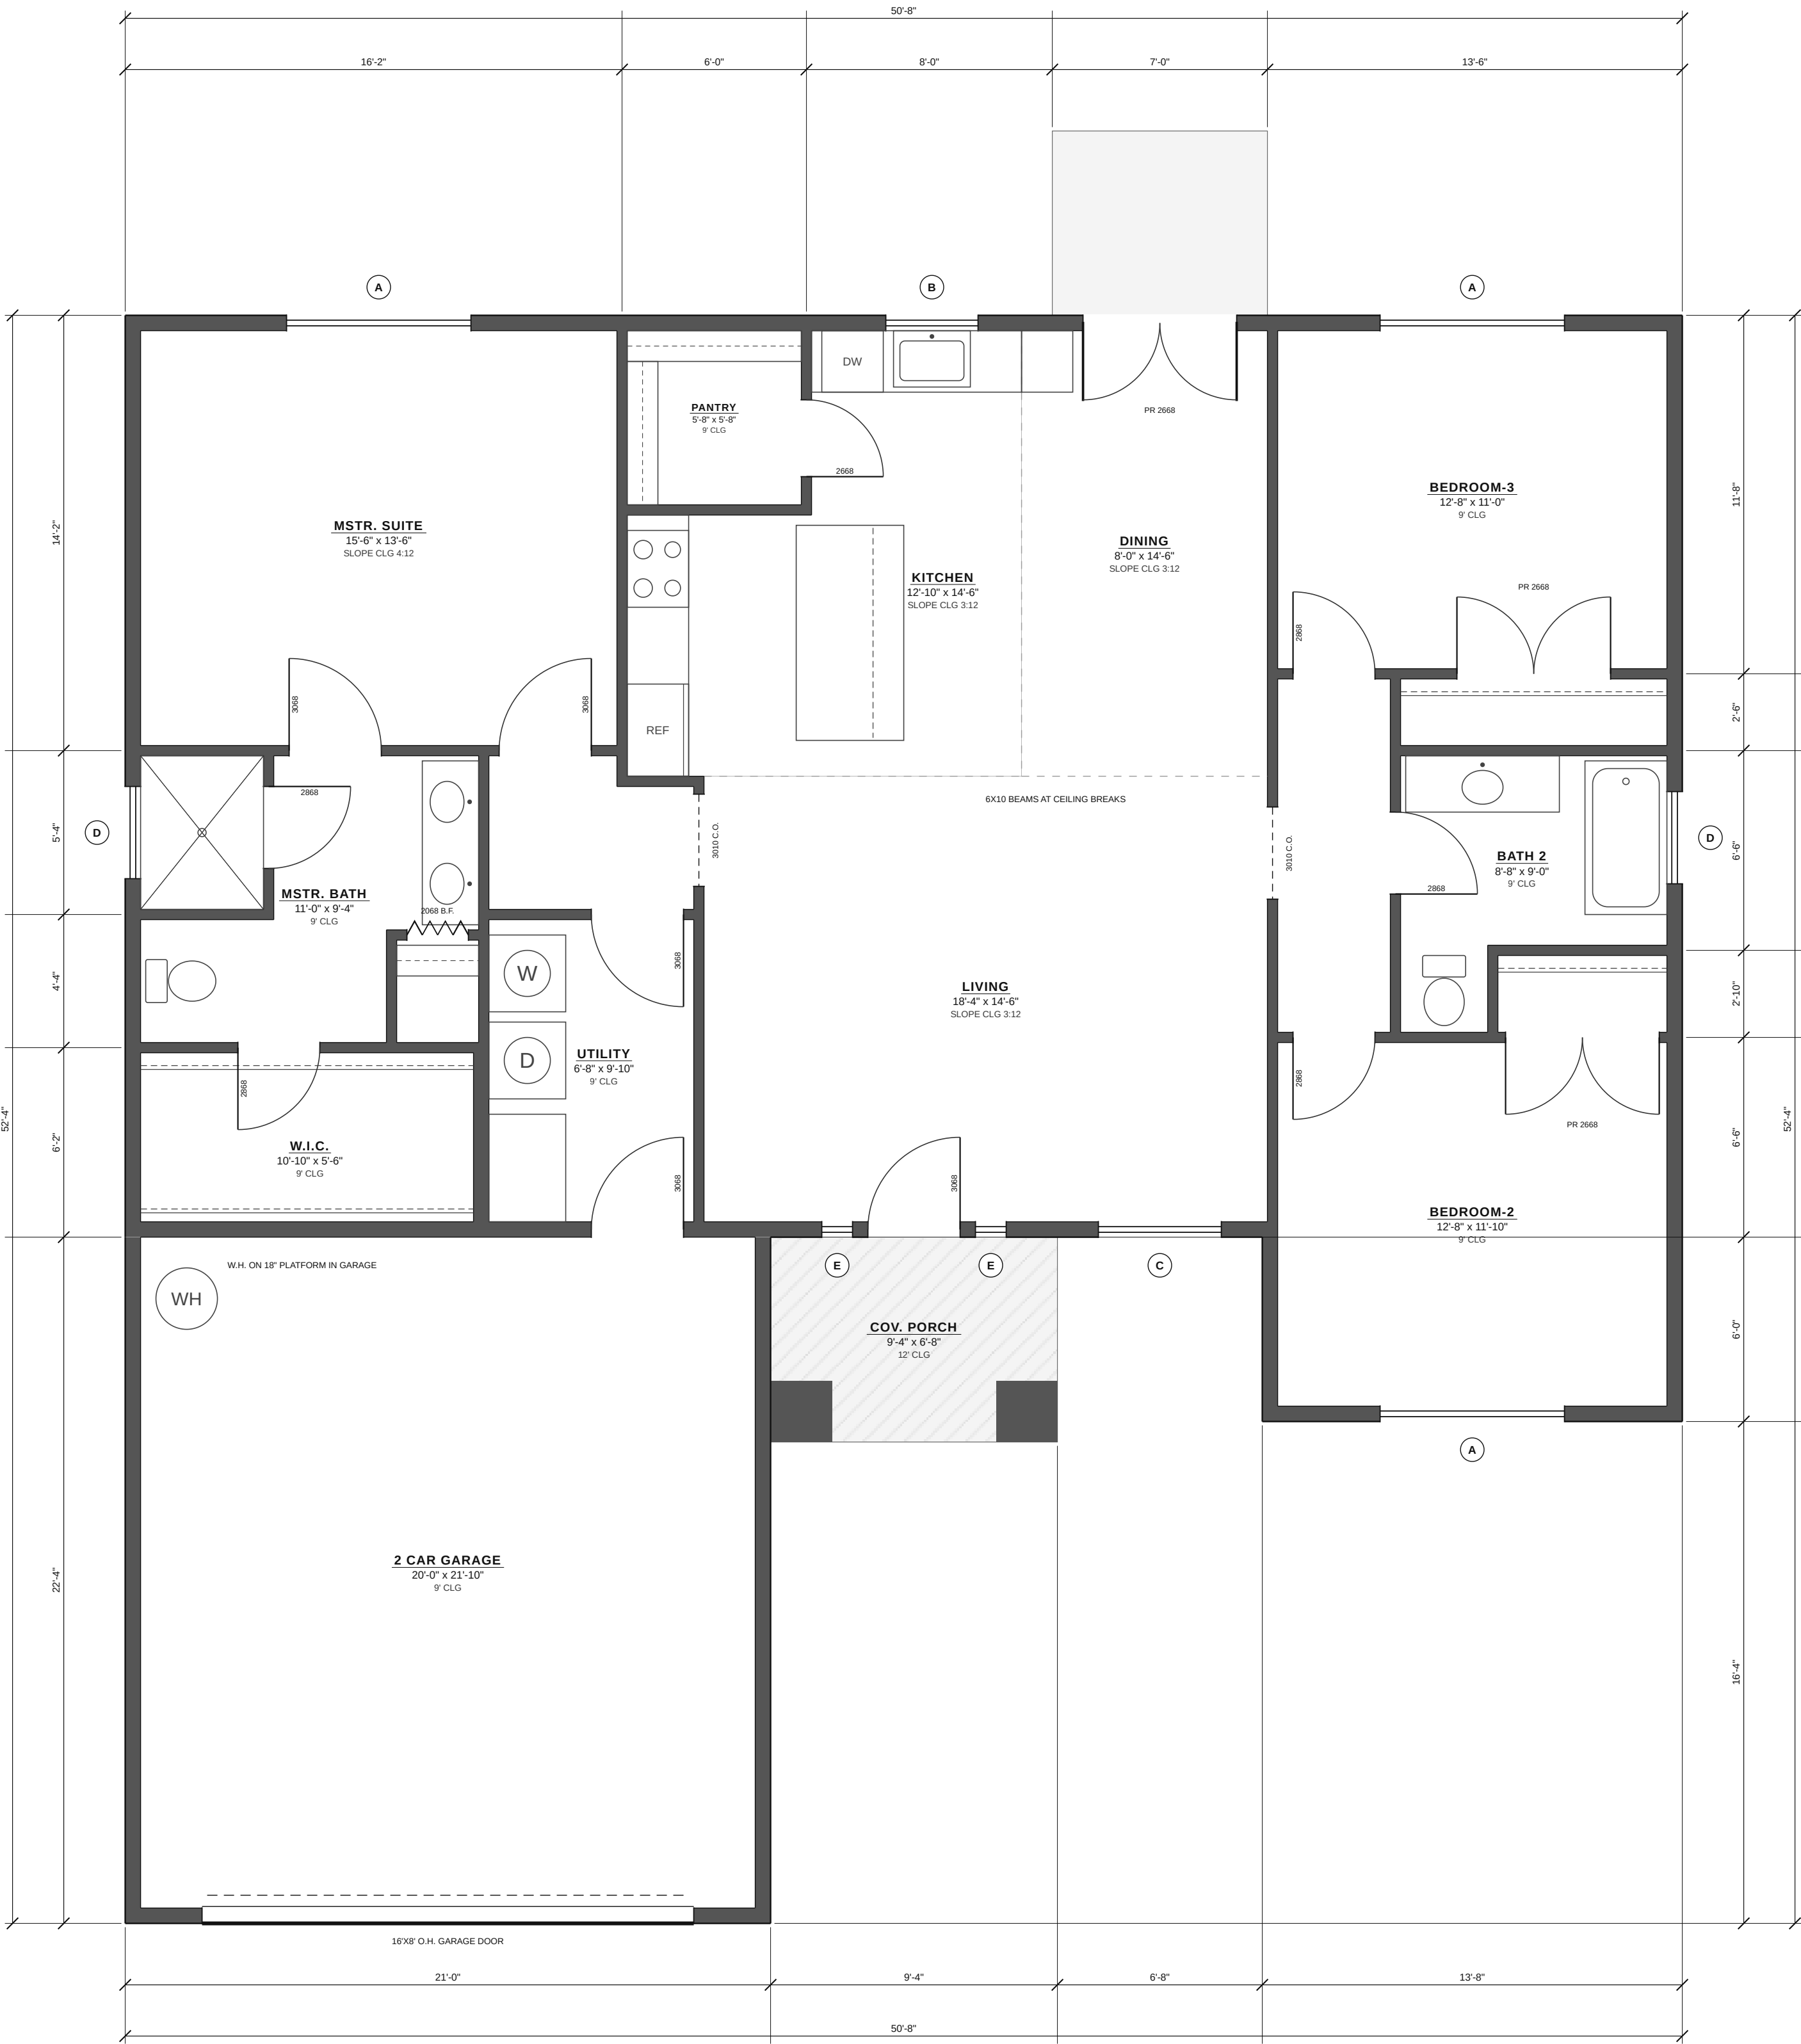


FLOOR PLAN
SCALE: 1/4" = 1'-0"


LIVING AREA	1,902 SF
GARAGE	469 SF
PORCH	62 SF
TOTAL UNDER ROOF	2,133 SF

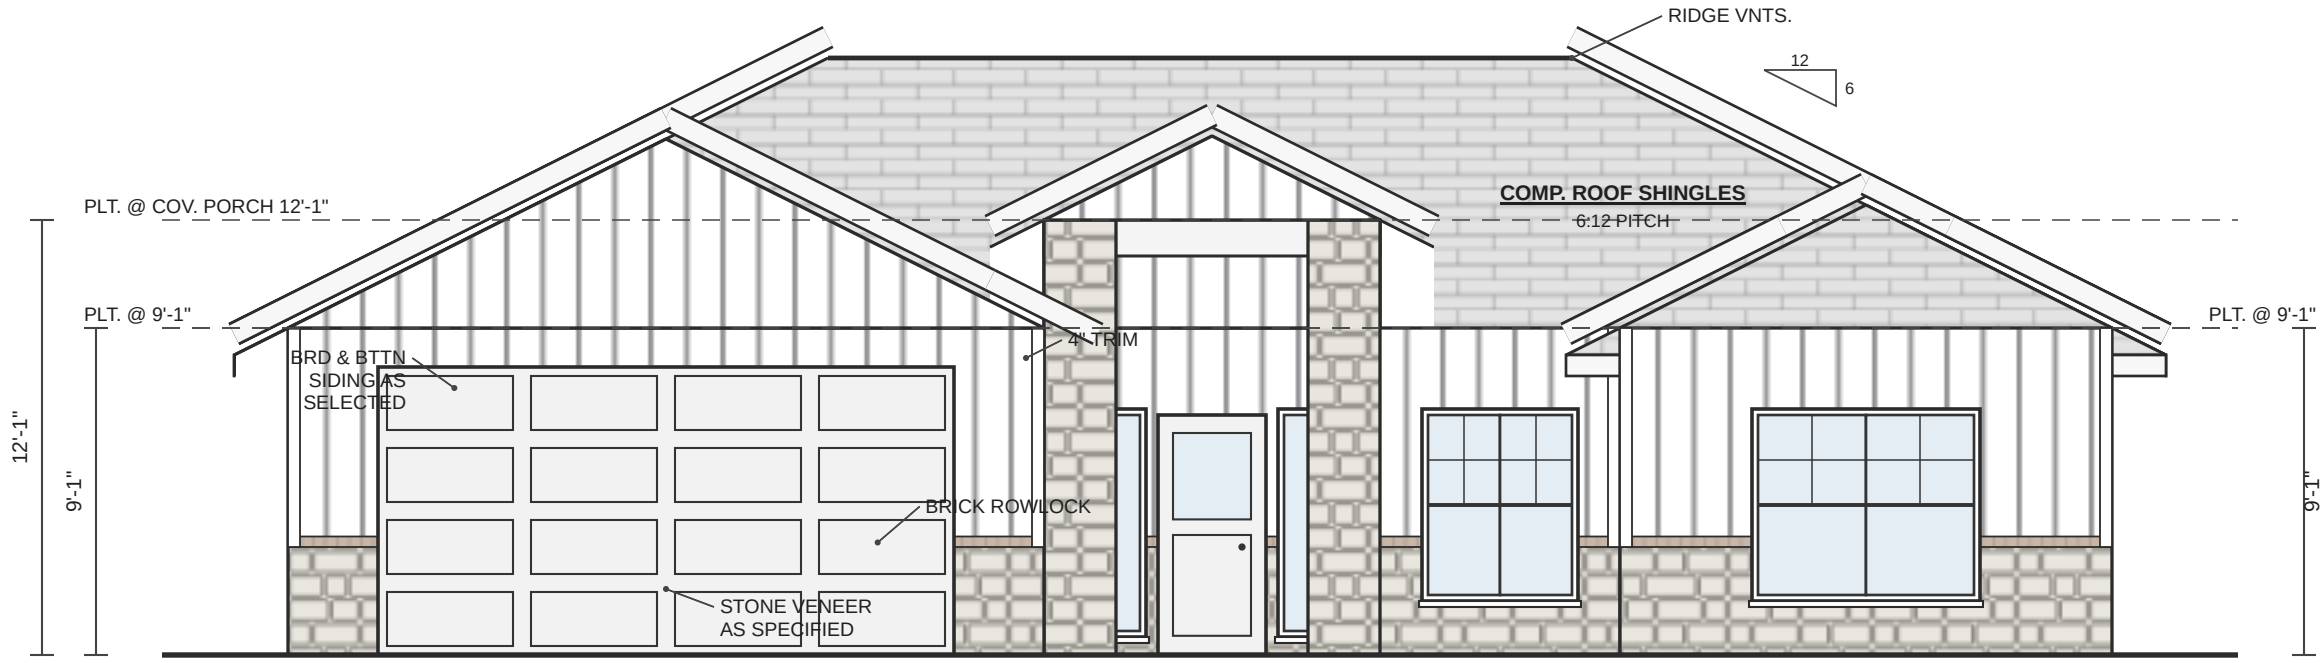


FRONT ELEVATION
SCALE: 3/16" = 1'-0"

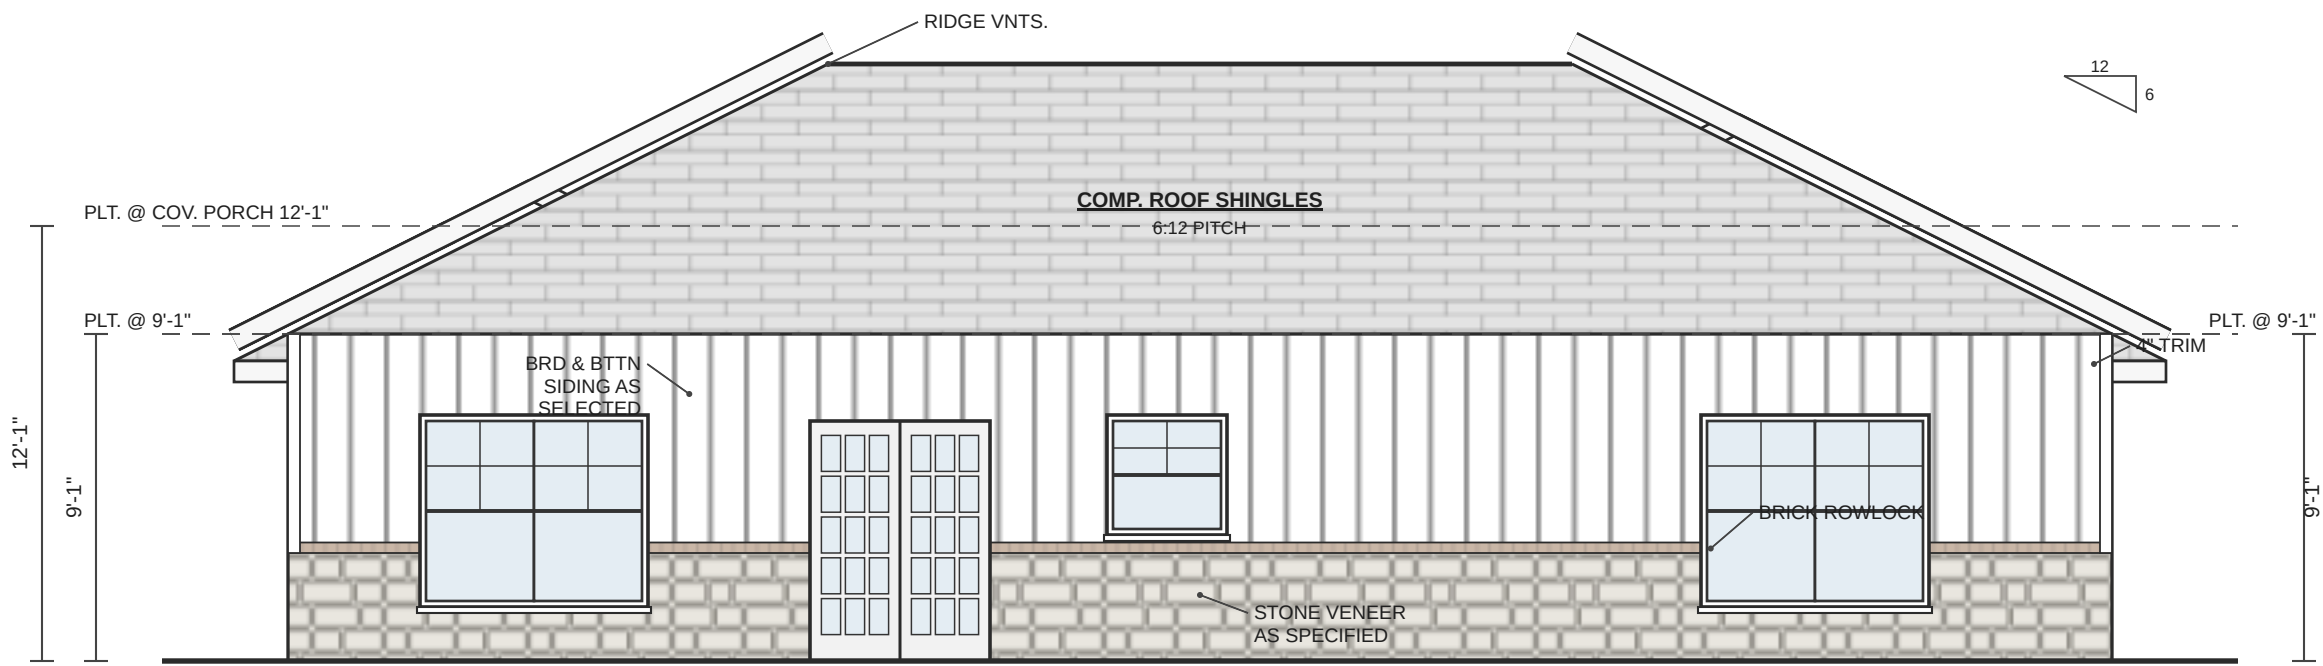

REAR ELEVATION
SCALE: 3/16" = 1'-0"

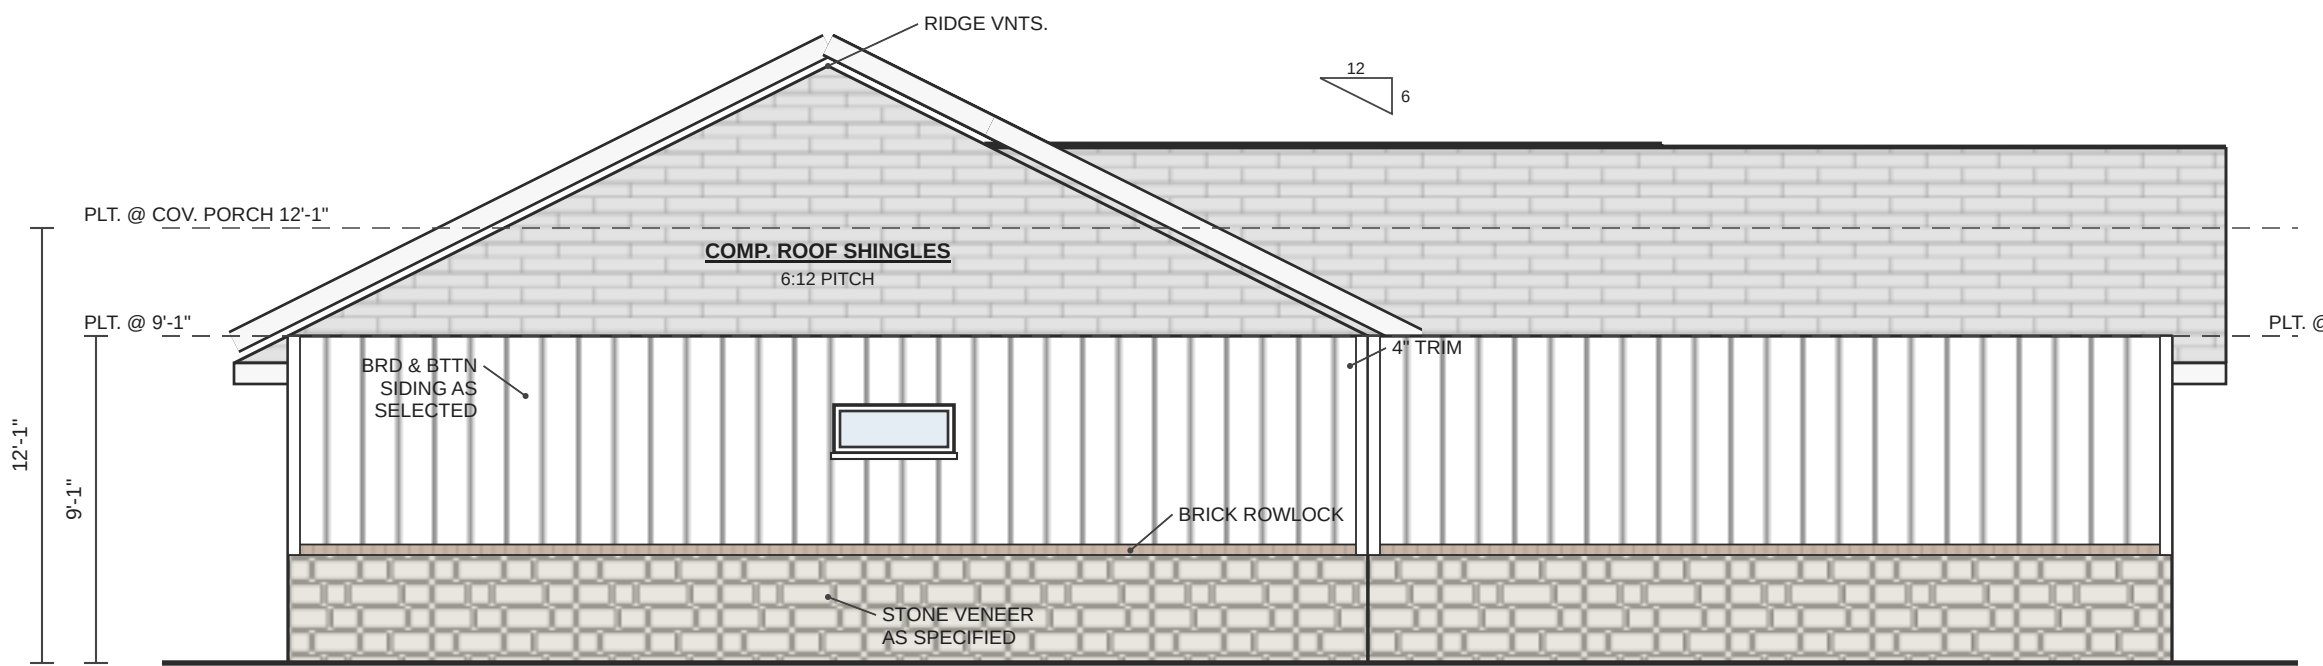

LEFT ELEVATION
SCALE: 3/16" = 1'-0"

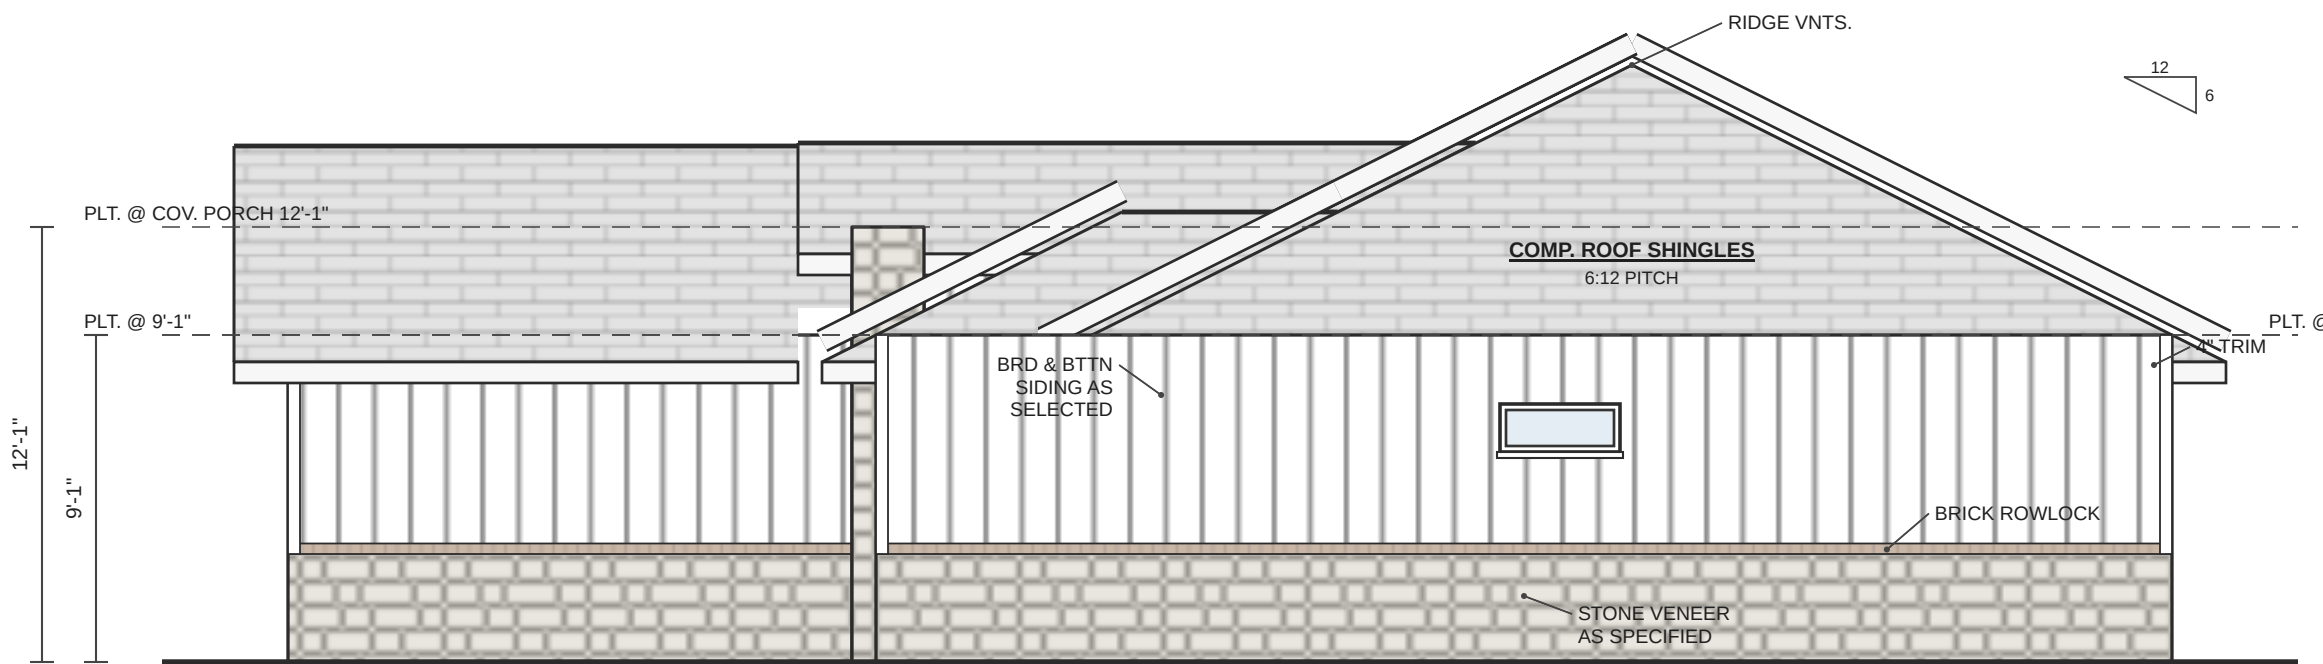

RIGHT ELEVATION
SCALE: 3/16" = 1'-0"

SF 1600 F

1,600 SF VARIANT OF SF 1258 F

CONCEPT STUDY
NOT FOR CONSTRUCTION

DERIVED FROM
Plan Factory plan SF 1258 "F" — designs by
Antonio Escobedo, San Antonio, TX (drawn
6/22/2023, plotted 10/10/2023). Permit
drawings must be prepared by the plan's
designer or a licensed designer/engineer.

PREPARED FOR
DANTEGA HOMES
DANIEL ORHIUNU
738 SAWTOOTH DR.
Lot 48 - Block 23 - N.C.B. 15850
Lackland City Subdivision
San Antonio, Bexar County, TX

SQUARE FOOTAGE TABULATIONS	
LIVING AREA	1,602
GARAGE	469
COV. PORCH	62
TOTAL UNDER ROOF	2,133
FLATWORK	479

FLOOR PLAN & ELEVATIONS

DATE
2026-09-04
GENERATED FROM
plans/sf1600/spec/sf1600.json - 2021 IRC
conventions carried from the original sheets